

HAZIRLAYAN



İDARE



YÜKLENİCİ


GENA

GENA İNŞAAT A.Ş.

PROJE ADI	Kars Harakani Havalimanı Pist Tadilatı
PROJE NUMARASI	DHMI-KRS-RGLSCD-R01
YAPAN	IDY Mühendislik Elektrik Elektronik San.Tic.Ltd.Şti.
PANO ADI	YENİ REGÜLATÖR BİNASI OG/AG RTU PANO PROJESİ

Oluşturma Tarihi	8.08.2023
Değiştirme Tarihi	19.07.2026

24

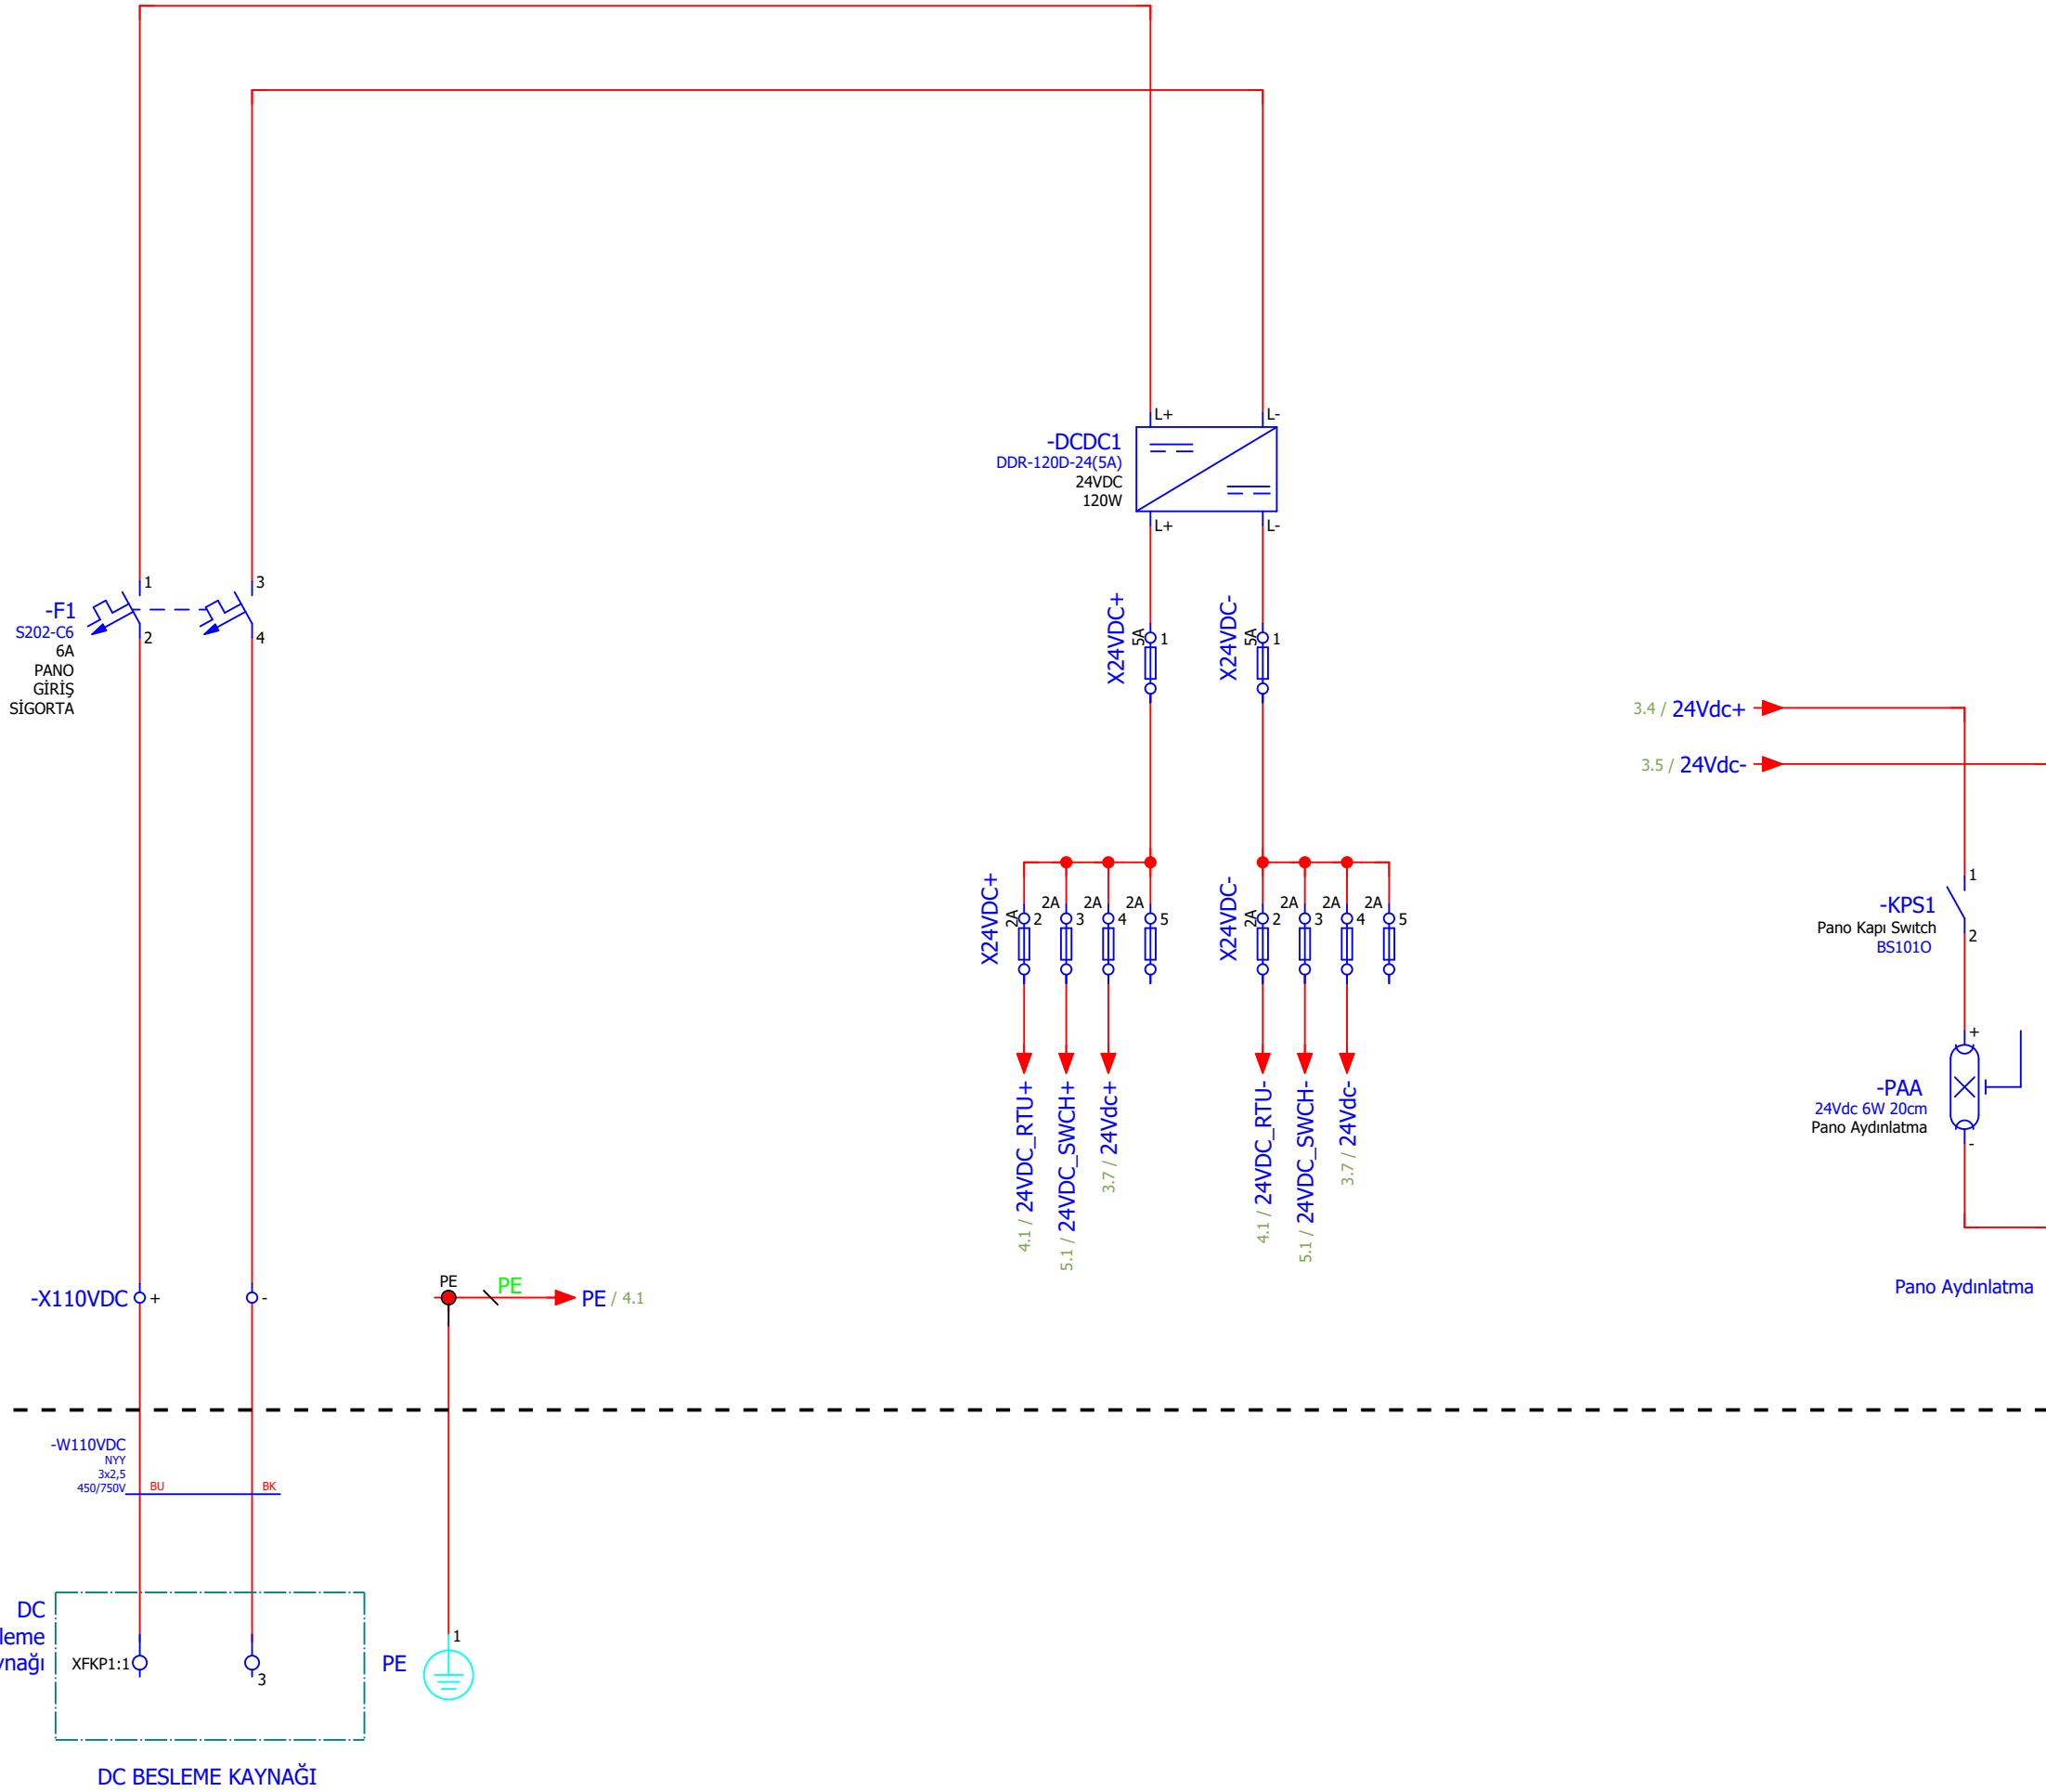


KABLO RENK KODU	
110VDC +	Turuncu
110VDC -	Gri
TOPRAK	Sarı/Yeşil
+24 Vdc	Kırmızı
GND	Siyah
SİNYAL	Beyaz

PANO


SAHA

IDY MUHENDİSLİK TÜM HAKLARI SAKLIDIR.

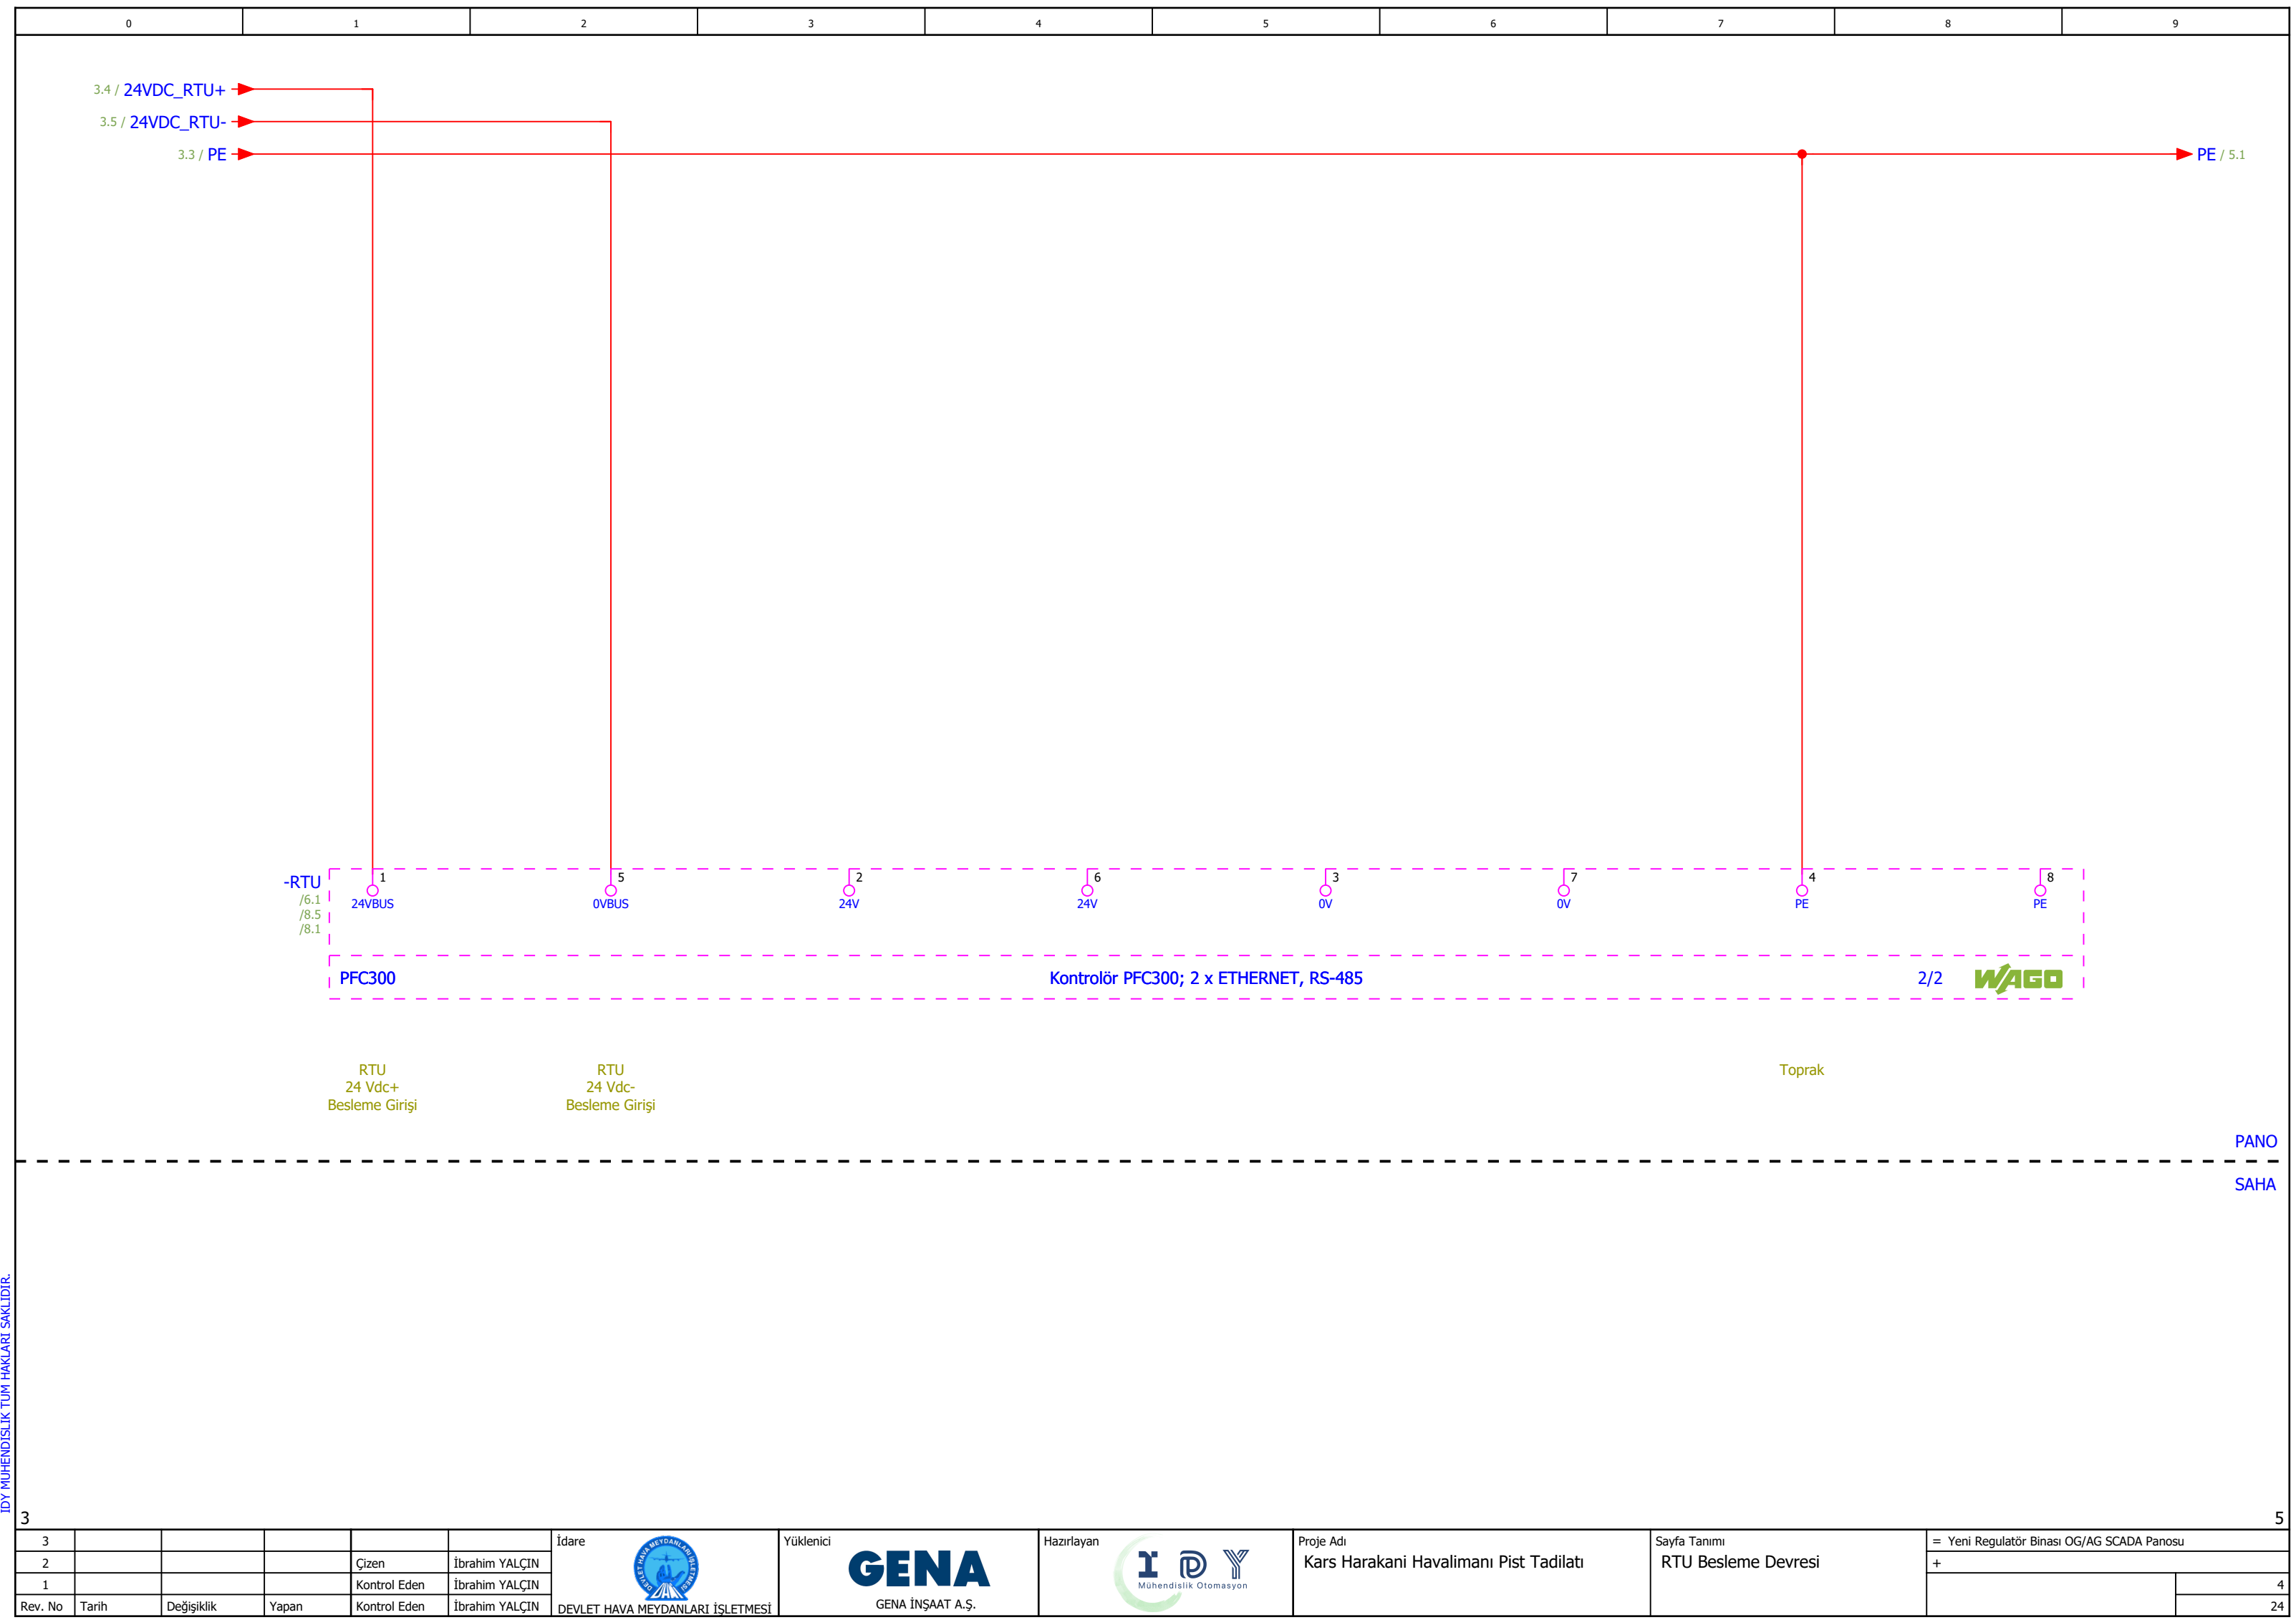

IDY MUHENDİSLİK TUM HAKLARI SAKLIDIR.

3						İdare		Yüklenici		Hazırlayan		Proje Adı	Sayfa Tanımı	= Yeni Regulator Binası OG/AG SCADA Panosu
2				Çizen	İbrahim YALÇIN							Kars Harakani Havalimanı Pist Tadilatı	RTU Besleme Devresi	+
1				Kontrol Eden	İbrahim YALÇIN									4
Rev. No	Tarih	Değişiklik	Yapan	Kontrol Eden	İbrahim YALÇIN	DEVLET HAVA MEYDANLARI İŞLETMESİ	GENA İNŞAAT A.Ş.							24

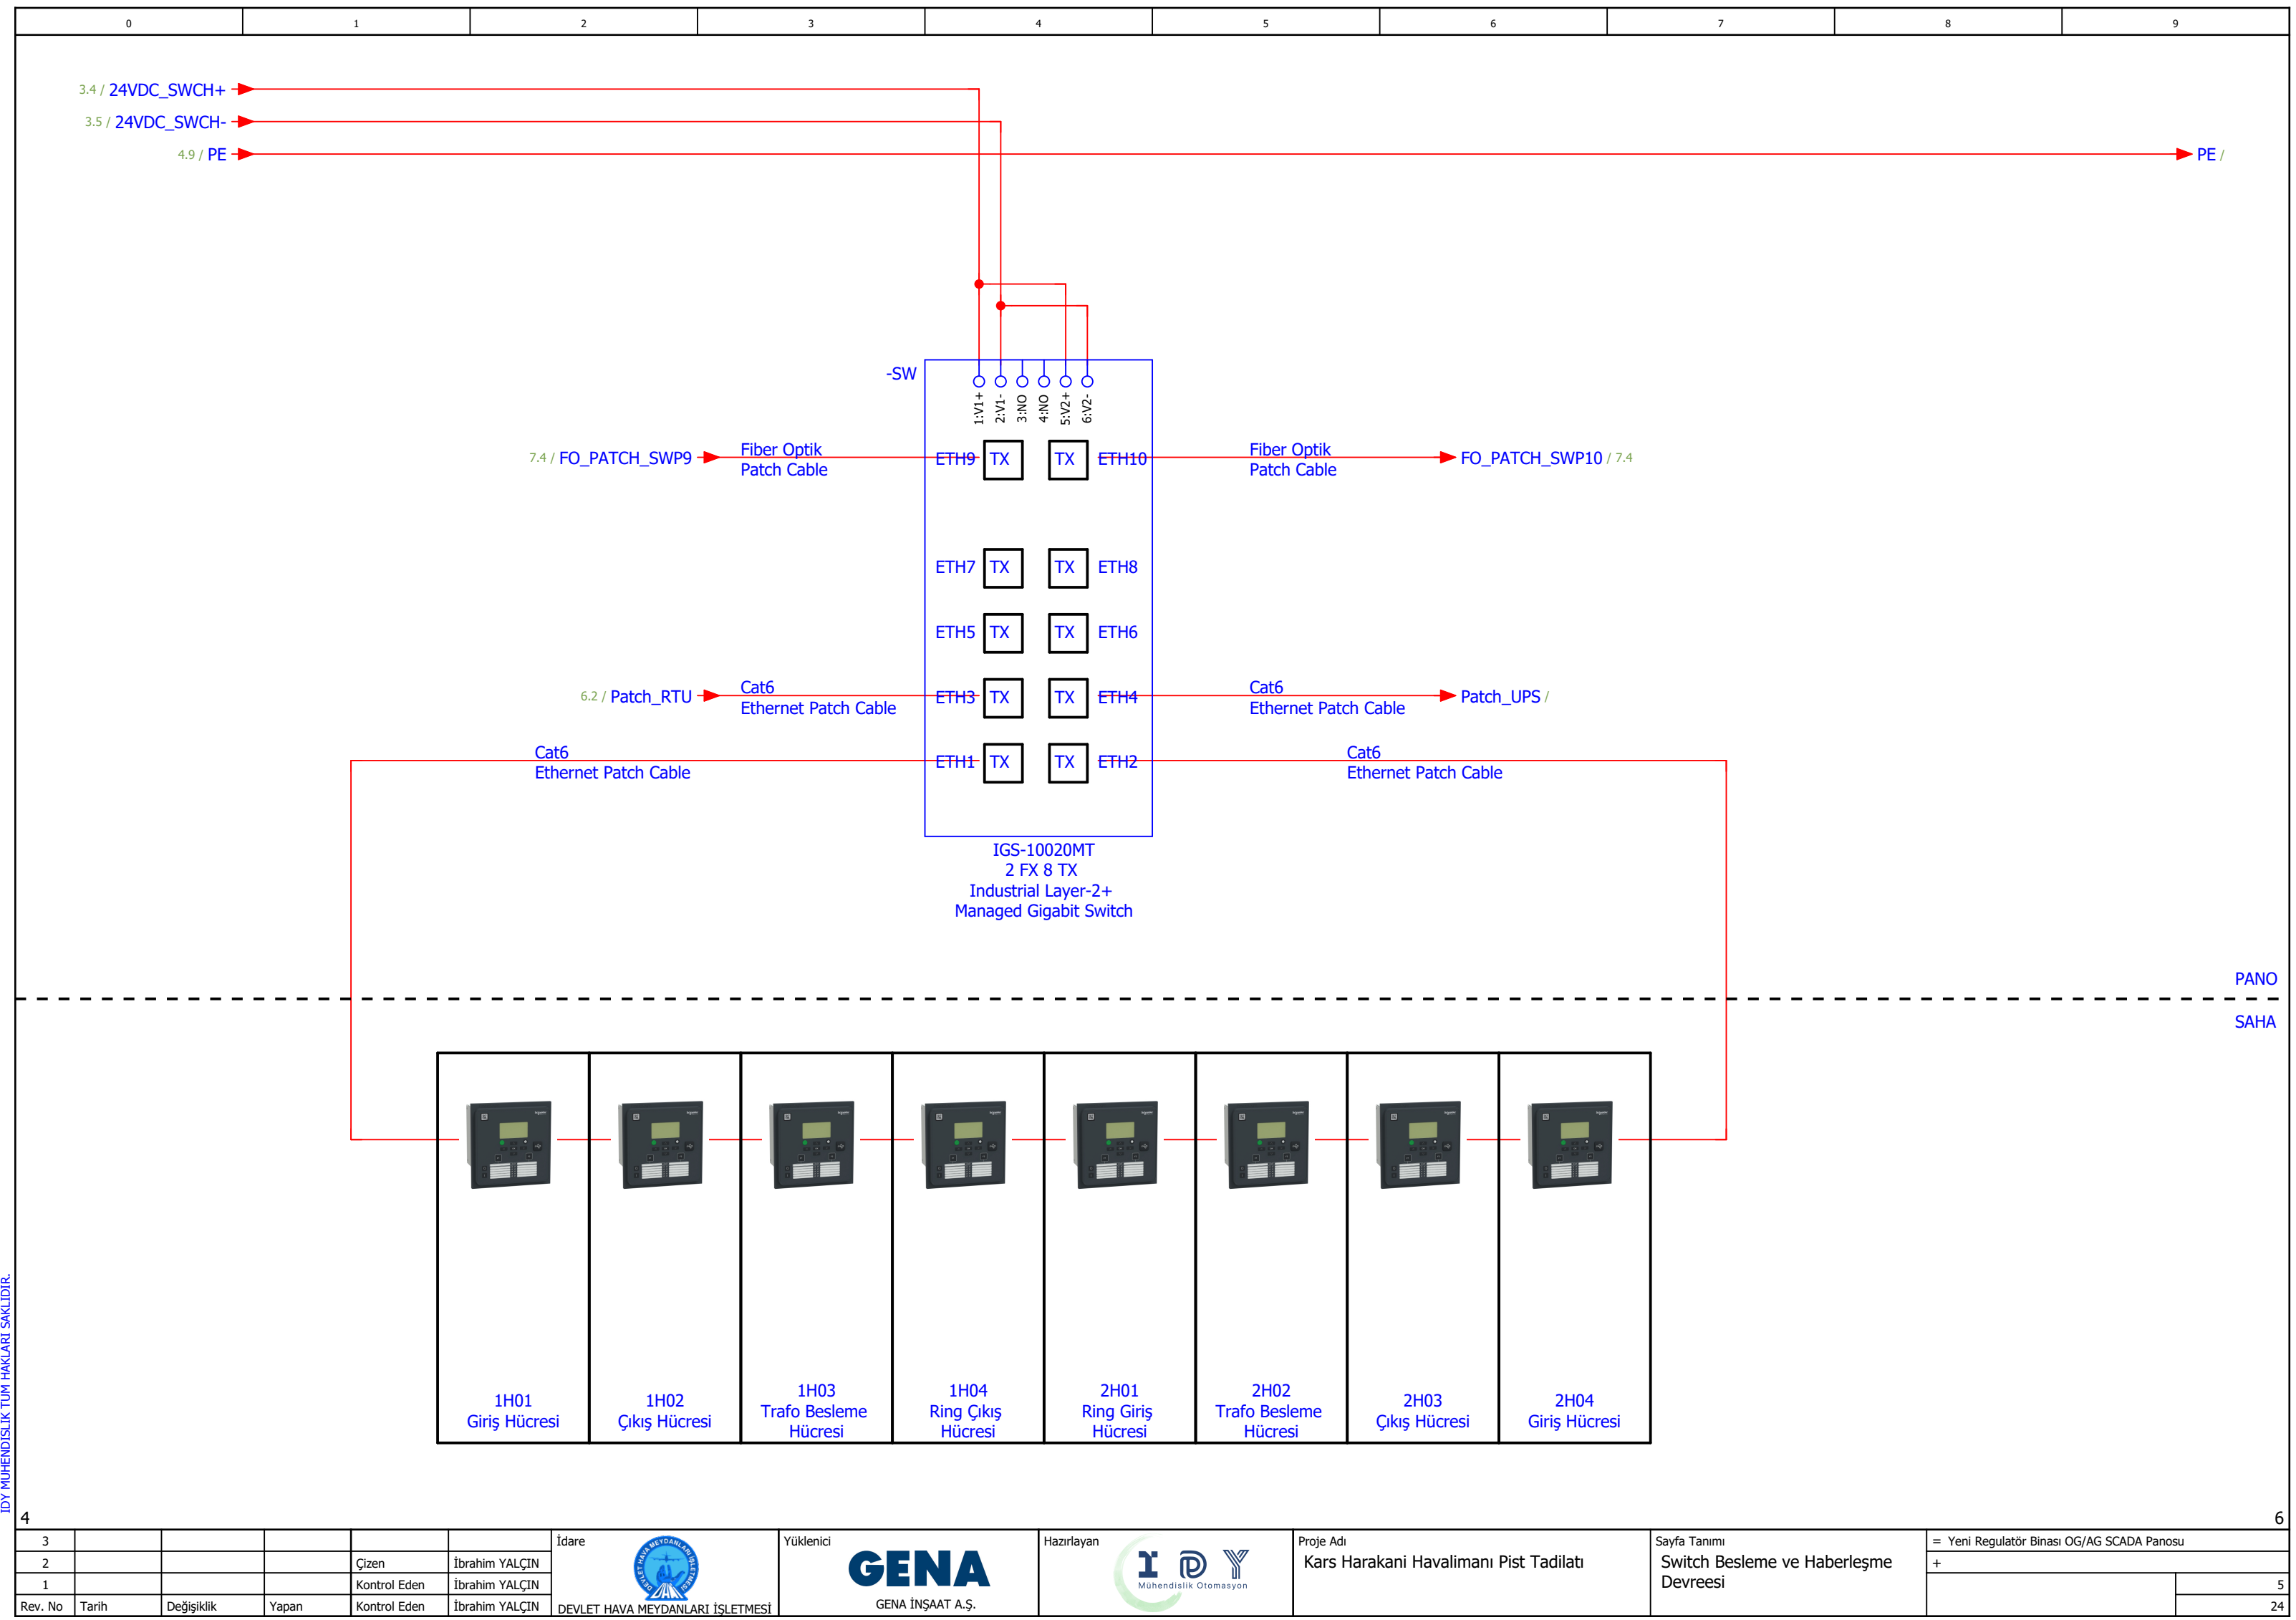


IDY MUHENDİSLİK TÜM HAKLARI SAKLIDIR.

AG ADP Giriş
Analizör Haberleşme

Switch Bağlantı
Ethernet

Yedek Ethernet
Port

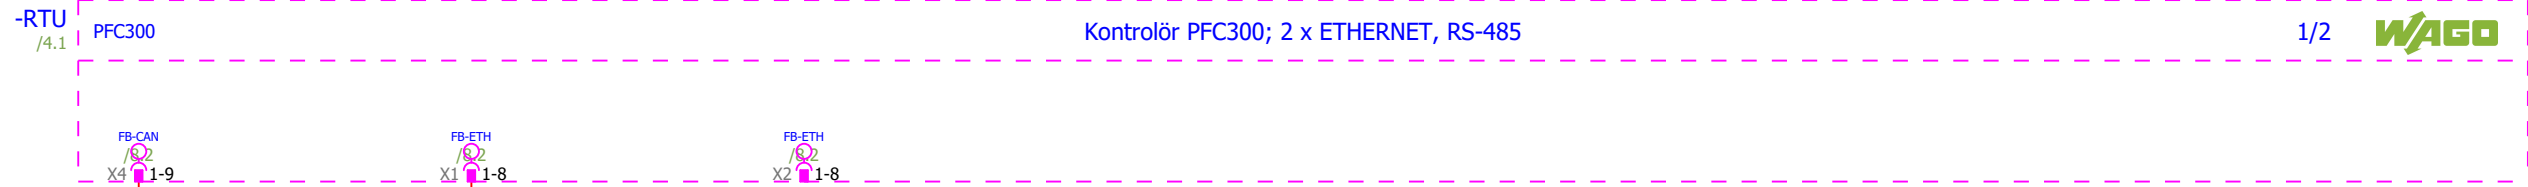

The communication interface is designed as a 9-pole SUB-D socket.

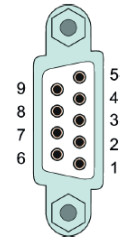


Figure 5: Communication Interface


Table 1: Pin Assignment of Communication Interface

Contact	RS-485	
	Signal	Description
1	NC	Not assigned
2	NC	Not assigned
3	A (Tx/Rx+)	Transmit/receive data +
4	NC	Not assigned
5	FB_GND	Ground
6	FB_5V	Power supply
7	NC	Not assigned
8	B (Tx/Rx-)	Transmit/receive data -
9	NC	Not assigned
Housing	Shield	Shield

The communication interface has a two-stage, on/off switchable bias network (1) and an on/off switchable bus termination resistor (2).

-XRS485 1 2 3

-WRS485_EA
RS-485
2x0,22

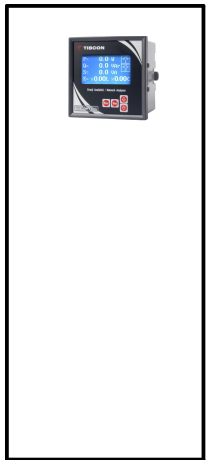

REGÜLATÖR BİNASI
ANA DAĞITIM PANOSU


PANO

SAHA

IDY MUHENDİSLİK TÜM HAKLARI SAKLIDIR.

Fiber Renkleri / Fiber Colours



No	1	2	3	4	5	6	7	8
Renk Colour	Mavi Blue	Turuncu Orange	Yeşil Green	Kahve Brown	Gri Grey	Beyaz White	Kırmızı Red	Siyah Black

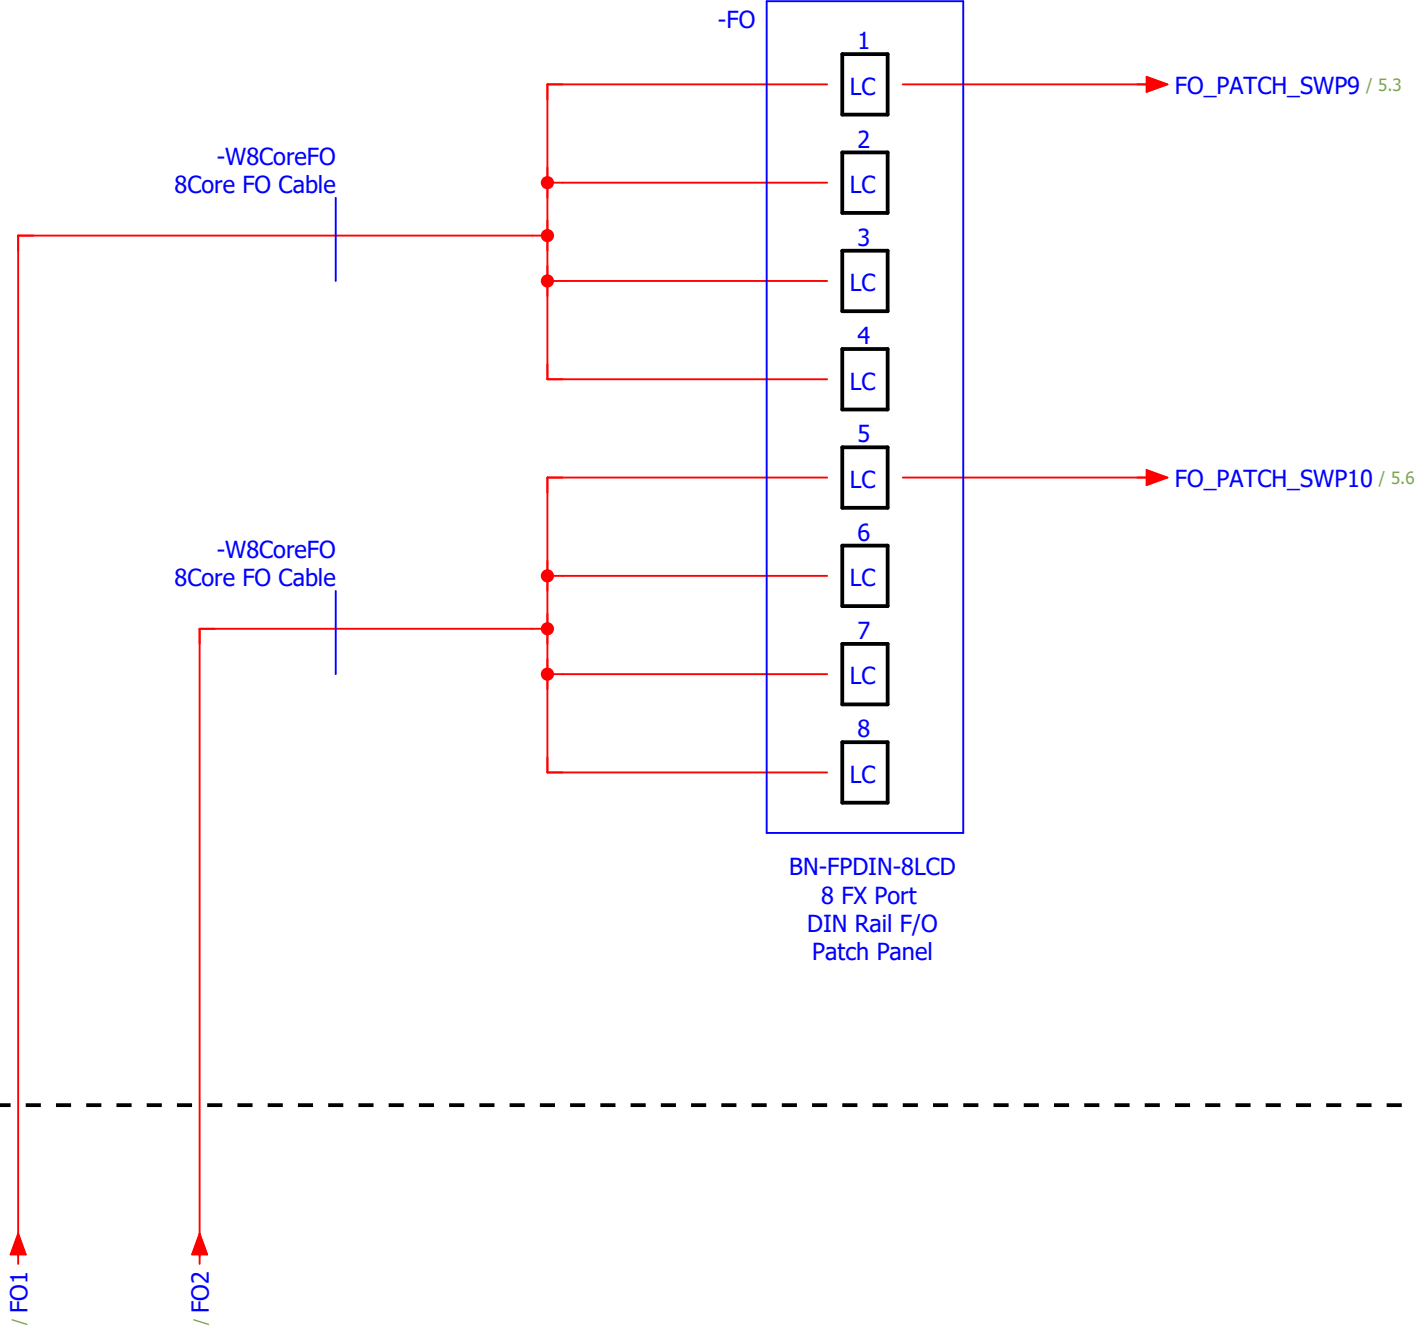

PANO

SAHA

IDY MUHENDİSLİK TÜM HAKLARI SAKLIDIR.

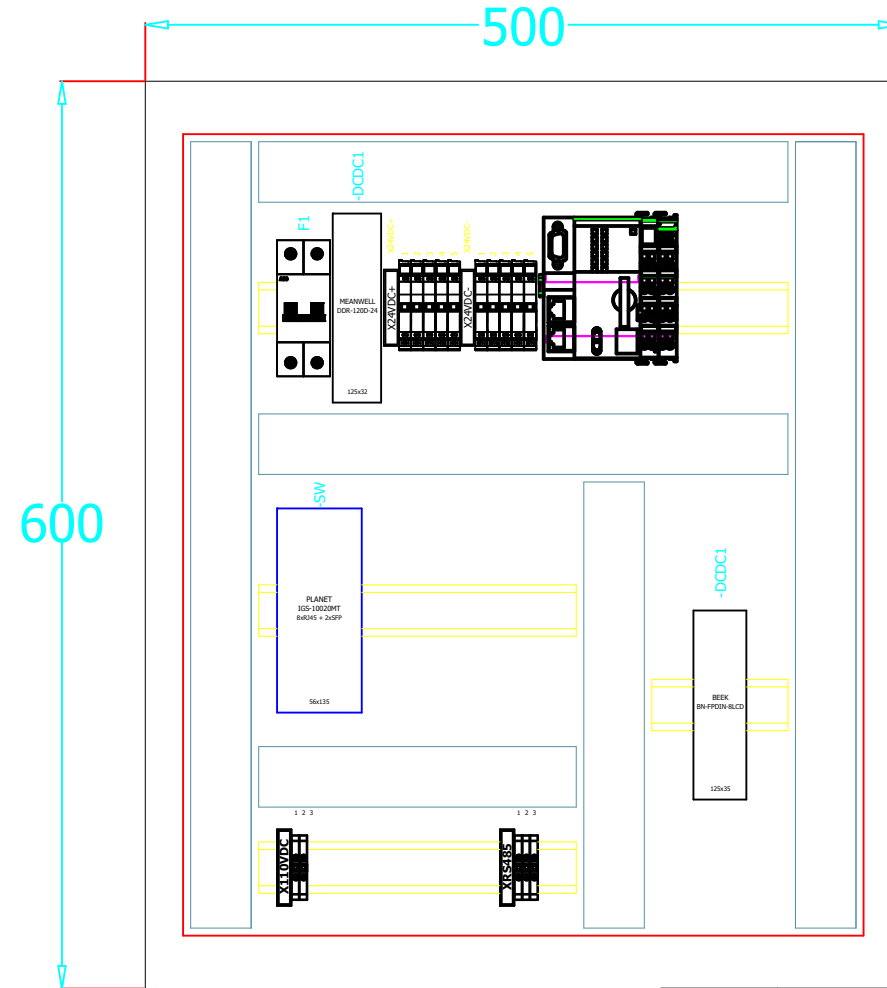 

3						İdare		Yüklenici		Hazırlayan		Proje Adı	Sayfa Tanımı	= Yeni Regulator Binası OG/AG SCADA Panosu	
2				Çizen	İbrahim YALÇIN							Kars Harakani Havalimanı Pist Tadilatı	Pano Yerleşim Planı	+	
1				Kontrol Eden	İbrahim YALÇIN										9
Rev. No	Tarih	Değişiklik	Yapan	Kontrol Eden	İbrahim YALÇIN	DEVLET HAVA MEYDANLARI İŞLETMESİ		GENA İNŞAAT A.Ş.							24



GENA
GENA İNŞAAT A.Ş.



IDY MUH_Malzeme_Listesi

ÜRÜN / SİPARİŞ NUMARASI	MİKTAR	AÇIKLAMA	ÜRÜN TİP NUMARASI
DDR-120D-24(5A)	1	DC/DC Güç Kaynağı, 110VDC/24VDC, 120W, 5A	DDR-120D-24
	0		
2CDS252001R0064	1	S 200-C eğrisi standart: IEC/EN 60898, IEC/EN 60947-2 Icn=6kA	S202-C6
BN-FPDIN-8LCD	1	Beek DIN-Ray için Ek Kutusu 8 x LC/Duplex	8 x LC/Duplex Coupler
EMAS.BS101O	1	1 NA, Ani Hareketli	BS101O
LED LIGHTING	1	24Vdc 6W 20cm	LED LIGHTING
750-8302	1	Kontrolör PFC300; 2 x ETHERNET, RS-485	PFC300
IGS-10020MT	1	Endüstriyel Tip 8-Port 10/100/1000T + 2 100/1000X SFP Managed Switch	PLANET_IGS-10020MT
150 100	10	DC4-HE-01P-11-00A(H) Sigortalı Klemens	DC4
150 000	5	DC2.5-01P-11-00A(H) Geçiş klemensi	DC2.5

IDY MUHENDİSLİK TUM HAKLARI SAKLIDIR.